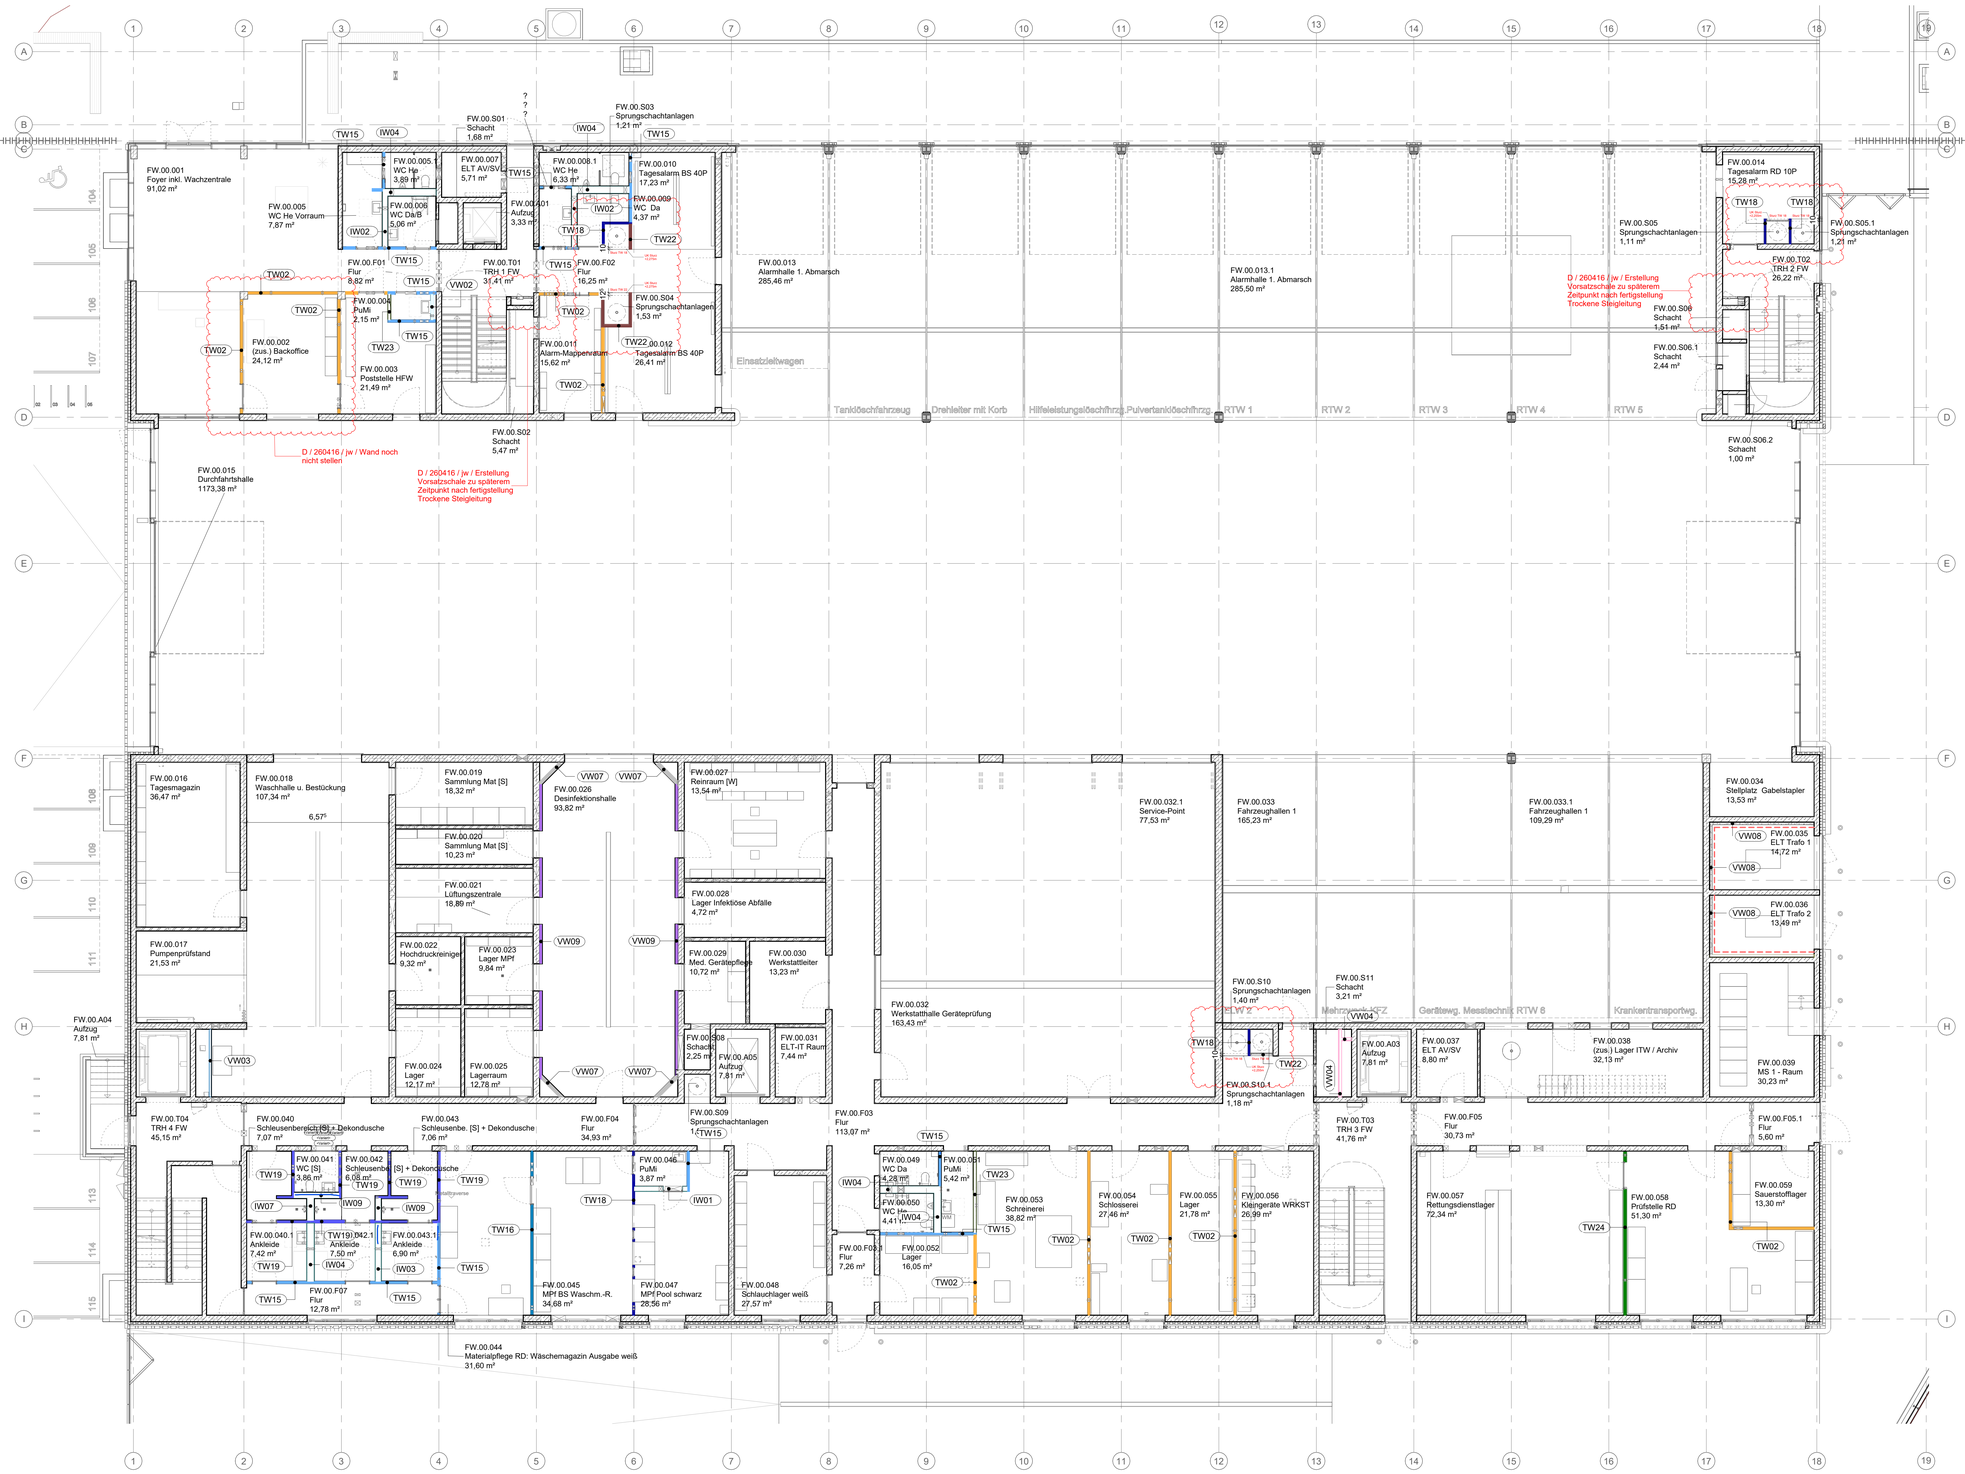


TROCKENBAU TRENNWÄNDE		TRENNWÄNDE im FEUCHT- UND NASSBEREICH	VORSATZWÄNDE SCHACHTWÄNDE WANDBEKLEIDUNG	INSTALLATIONS-WÄNDE
TW 01 | 100mm	TW 09 | 125mm	TW 15 | 125mm	VW 01 | 100mm	IW 1 - 15 | 245 - 385mm
TW 02 | 125mm	TW 10 | RC2 125mm	TW 16 | 125mm	VW 02 | 100mm	
TW 03 | 125mm	TW 11 | RC3 127mm	TW 17 | 125mm	VW 03 | 100mm	
TW 04 | 125mm	TW 12 | 125mm	TW 18 | 100mm	VW 04 | 115mm	
TW 05 | 125cm	TW 13 | 116mm	TW 19 | 125mm	VW 05 | 100mm	
TW 06 | 125mm	TW 14 | 126mm	TW 20 | 125mm	VW 06 |	
TW 07 | 125mm	TW 22 | 125mm	TW 21 | 125mm	VW 07 | 100mm	
TW 08 | 100mm	TW 24 | 150mm		VW 08 | 125mm zementgebundene HWL Platten mit Dämmeinlage	
			VW 09 | 120mm	

Index	Änderungsbeschreibung	Datum	Gez.	Gepr.
D	Planung Trockenbau fortgeschrieben	15.07.2026	wa	

Objekt

Hauptfeuerwache mit Rettungswache
An den Kaiserthermen 1, 54290 Trier

und Integrierte Leitstelle
An den Kaiserthermen 3, 54290 Trier

Planinhalt

FWT EG Trockenbauwände

Maßstab: 1:100
Datum: 15.07.2026
Gezeichnet: sbr
Plannummer - wa: 573
Geprüft: sbr
Plannummer - Dateinamenskonvention: HFW_F_5_039.1_00_UE_02_F- D
Projektstatus: Ausführungsplanung
Format: 1189 x 841mm

Entwurfsverfasser
wulf architekten gmbh
Breitscheidstraße 8
70174 Stuttgart
t +49 711 248 917-0
wulf architekten
Datum, Unterschrift Entwurfsverfasser

Generalplaner / Architekt
wulf architekten gmbh
Breitscheidstraße 8
70174 Stuttgart
t +49 711 248 917-0
wulf architekten
Datum, Unterschrift Generalplaner:in / Architekt:in

Bauherr
Stadtverwaltung Trier - Amt für Brand-, Zivilschutz und Rettungsdienst
St. - Barbara - Ufer 40
54290 Trier
t 0651 9488 - 0
f 0651 9488 - 1901
TRIER
Datum, Unterschrift Projektmanagement
Datum, Unterschrift Amtsleitung
Datum, Unterschrift Dezernat