




flächige Verstärkung in Trockenbauwand Stahlblech für Werkstatträume oä, Feucht und Nassraumgeeignet

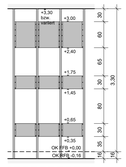


Verstärkungstraversen Trockenbauwand mit Brandschutzanforderungen, Stahlblech in Ruheräumen

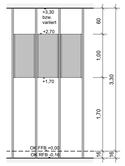


Verstärkung in Trockenbauwand Stahl zB für Alarmmonitore in Fluren

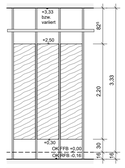


flächige Verstärkung in Trockenbauwand OSB für Besprechungsräume, Sportraum, LuK, ELZ

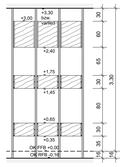


Verstärkungstraversen Trockenbauwand Holz Schrankwand in Ruheräumen ohne Brandschutzanforderung aus Holz in den Ruheräumen

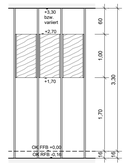


Verstärkungstraversen Trockenbauwand Holz z.B für Alarmmonitore in Fluren, Büroräume

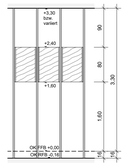


Verstärkungstraversen Trockenbauwand Holz Wandblechhme zB in Ruheräumen

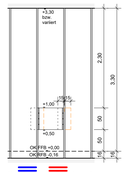


Verstärkungstraversen Trockenbauwand für Feuerlöscher: Holz (blau) Stahl (rot)

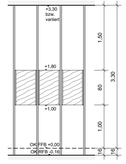


Verstärkungstraversen Trockenbauwand Holz Wandblechhme Aufenthaltsräume

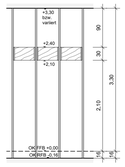

Verstärkungstraversen Trockenbauwand für Hochschränke Einbauort: FWT OG 2, FWT OG 3, ILTS

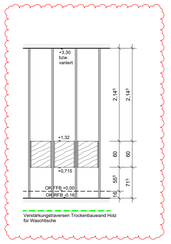

Verstärkungstraversen Trockenbauwand Holz für Waschtische

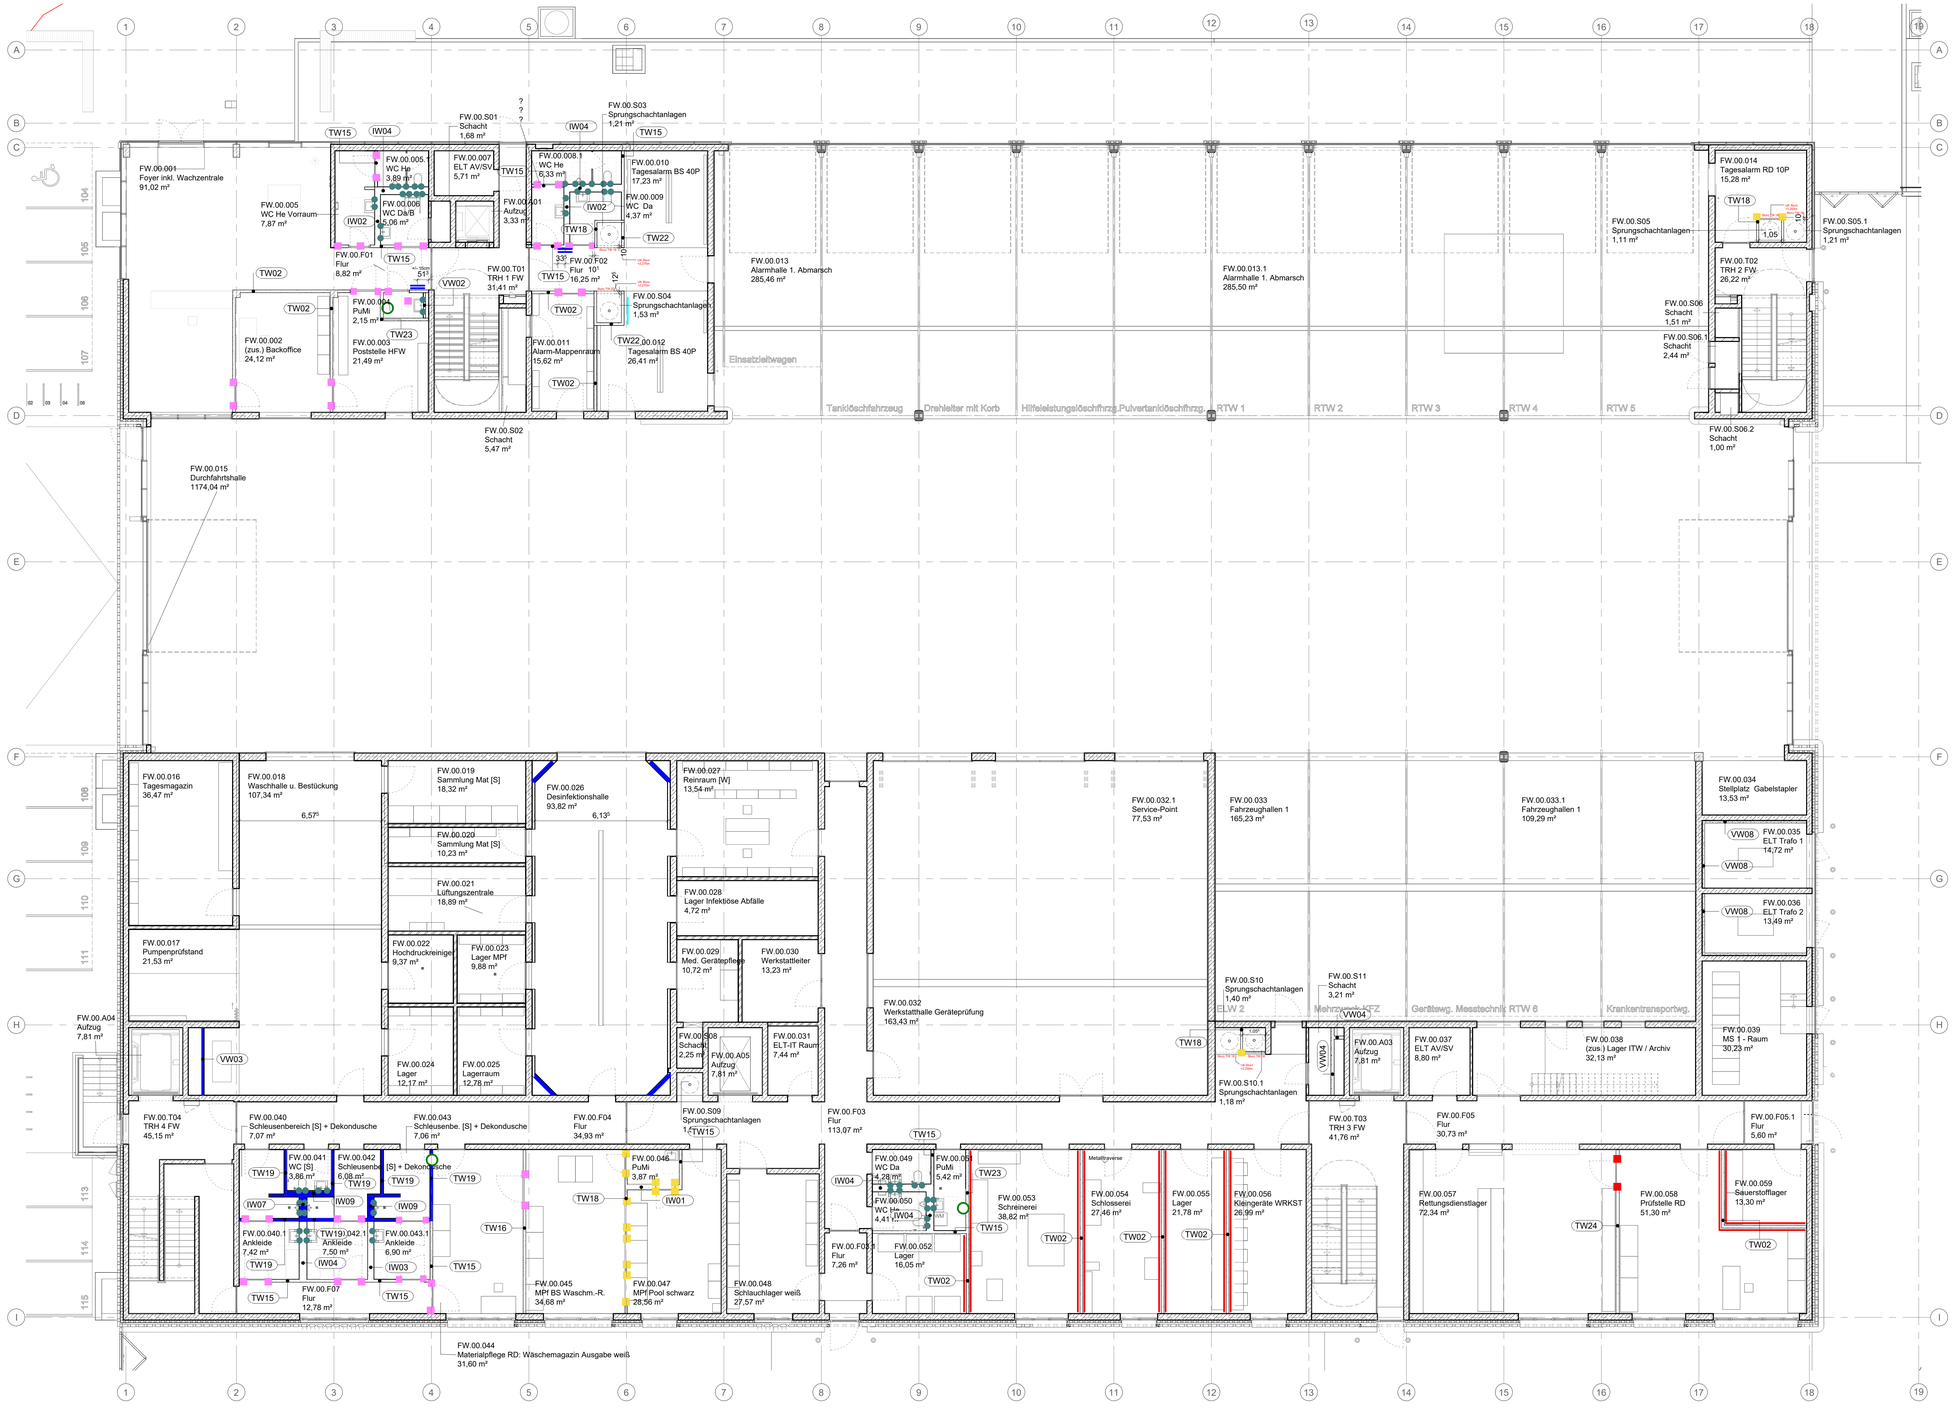

WANDVERSTÄRKUNGEN

Stahlblech

- Verstärkungstraversen Trockenbauwand mit Brandschutzanforderungen, Stahlblech
- flächige Verstärkung in Trockenbauwand Stahlblech für Werkstatträume oä, Feucht und Nassraumgeeignet
- Verstärkung in Trockenbauwand Stahlblech für zb Alarmmonitore Feucht und Nassraumgeeignet

Holz

- Verstärkungstraversen Trockenbauwand Holz Schrankwand in Ruheraum
- Verstärkungstraversen Trockenbauwand Holz Wandbildschirme in Ruheräumen / Besprechern
- Verstärkungstraversen Trockenbauwand Holz Flächig, Besprecher, Fitnessraum
- Verstärkungstraversen Trockenbauwand Holz Aufenthaltsräume
- Verstärkungstraversen Trockenbauwand Holz für zB. Alarmmonitore in Fluren
- Verstärkungstraversen Trockenbauwand Holz für Hochschränke
- Verstärkungstraversen Trockenbauwand Holz für Waschtische
- Verstärkungstraversen Trockenbauwand Holz Feuerlöscher
- Verstärkungstraversen Trockenbauwand Stahl Feuerlöscher

TROCKENBAUSTÜRZE

- ST 01 | 126mm, F60 + M (Aufbau TW 14)
- ST 02 | 125mm, F60 (Aufbau TW 12)
- ST 03 | 125mm, F60 (Aufbau TW 06)
- ST 04 | 125mm, F30 (Aufbau TW 05)
- ST 05 | 100mm, F60 (Aufbau TW 08)

Korrosivitätskategorie C3 der Unterkonstruktion

PROFILVERSTÄRKUNGEN

Profile

- Verstärkung Stahlhohlprofil, 50mm x 50mm
- Verstärkung Stahlhohlprofil, 75mm x 75mm
- Verstärkung Stahlhohlprofil, 100mm x 100mm
- Verstärkung Stahlhohlprofil, 75mm x 50mm
- Verstärkung für Sanitärinstallationen, WC Trennwände | UA-Profil
- Verstärkung für Waschtische, Stahlhohlprofile

REVISIONSÖFFNUNG

- Revisionsöffnung in der Wand 40cm x 60cm
- Revisionsöffnung in der Wand 60cm x 80cm
- Heizkreisverteiler mit Klappe

ANSCHLÜSSE

Gleitende Deckenanschlüsse horizontal siehe Übersicht zu den Deckendurchhängungen HFW_F_5_039.1_XX_SM_01 bis SM_10

Anschlüsse vertikal an Stahlbetonwände: starrer Wandanschluss

Anschlüsse horizontal an Brettsperrholzaußenwände: gleitender Wandanschluss

Index	Änderungsbeschreibung	Datum	Gez.	Gepr.
F	Planung Trockenbauverstärkungen fortgeschrieben	18.08.2026	wa	

Objekt

Hauptfeuerwache mit Rettungswache
An den Kaiserthermen 1, 54290 Trier

und Integrierte Leitstelle
An den Kaiserthermen 3, 54290 Trier

Planinhalt

FWT EG Trockenbauverstärkung

Entwurfsverfasser

Datum, Unterschrift Entwurfsverfasser

Generalplaner / Architekt

Datum, Unterschrift Generalplaner:in / Architekt:in

Bauherr

Stadtverwaltung Trier - Amt für Brand-, Zivilschutz und Rettungsdienst
St. - Barbara - Ufer 40
54290 Trier
t 0651 9488 - 0
f 0651 9488 - 1901

Datum, Unterschrift Projektmanagement

Datum, Unterschrift Amtsleitung

Datum, Unterschrift Dezernat

Maßstab 1:100	Datum 15.07.2026
Gezeichnet sbr	Plannummer - wa 627
Geprüft sbr	Plannummer - Dateinamenskonvention HFW_F_5_039.1_00_UE_12_F- F
Projektstatus Ausführungsplanung	
Format 1189 x 841mm	