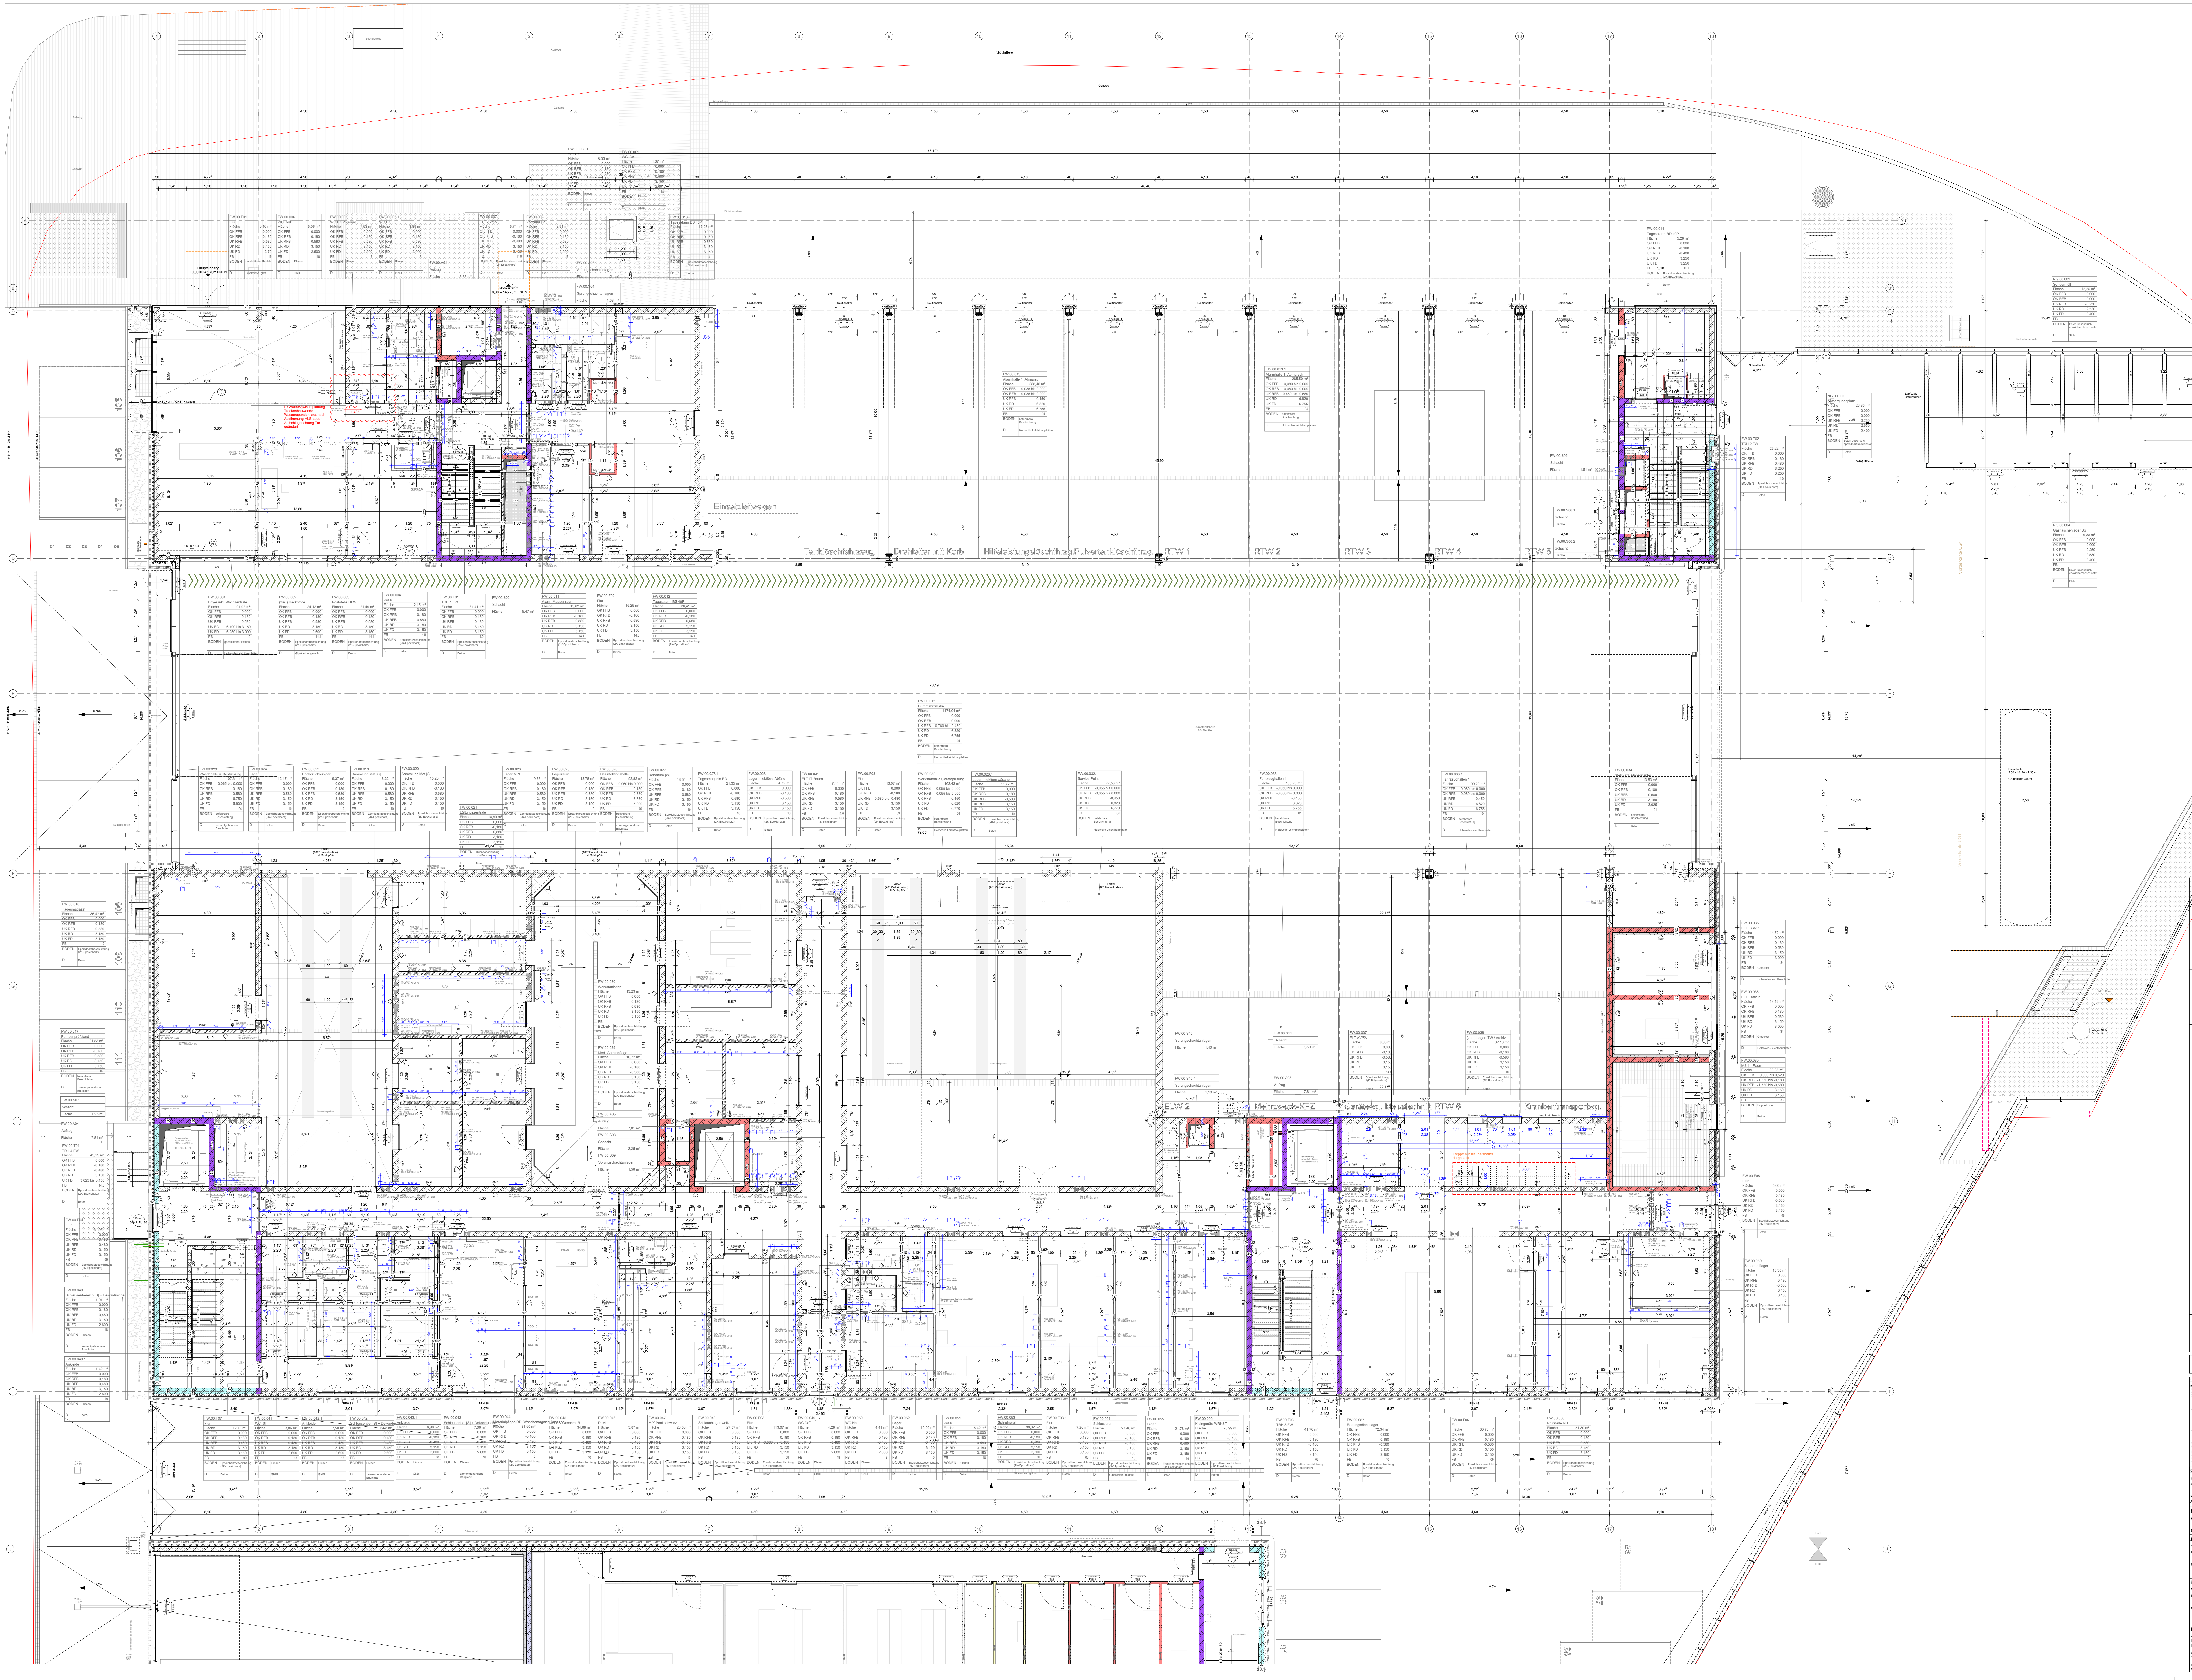

LEGENDE

STB	Stahlbeton	MW Z	Mauerwerk, Ziegel	MW KS	Mauerwerk, Kalksandstein
STB WU	Stahlbeton WU	GK	Montagewand, Gipskarton		Grundstücksgrenze
BFT	Stahlbeton-Fertigteil	H	Brettschichtholz, Konstruktionsholz		Dämmziegel

AUSSPARUNGEN

DD (L/B)	Deckendurchbruch	BD (L/B)	Bodendurchbruch
DS (L/B/H)	Deckenschlitz	BS (L/B)	Bodenschlitz
DD (L/B)	Wanddurchbruch - Freigegeben	KB (⌀)	Kernbohrung Boden
DD (L/B)	Wanddurchbruch - ohne Freigabe		
SWS/WWS (L/B/H)	Senkrecher/ Waagrechter Wandschlitz	KB (⌀)	Kernbohrung Decke

SYMBOLE SCHNITT

RFB	Rohfußboden
FFB	Fertigfußboden
RFB = FFB	Rohfußboden = Fertigfußboden
UK RD	Unterkante Rohdecke
UK FD	Unterkante Fertigdecke
UK RD = UK FD	Unterkante Rohdecke = Unterkante Fertigdecke

SYMBOLE GRUNDRISS

VK RD	Vorderkante Rohdecke
VK FD	Vorderkante Fertigdecke
Höhenkote	FFB RFB
Detailverweis	DET --- Detail Detailnummer

ABKÜRZUNGEN

AK	Aussenkante	LH	Lichte Höhe
B ...	Boden	NRWG	Natürliches Rauch- und Wärmeabzugsgerät
BA	Bodenablauf	OK	Oberkante
BRH	Brüstungshöhe ab FFB	RA	Öffnung zur Rauchableitung
D ...	Decke	RH	Rohhöhe
DE	Dacheinlauf	RR	Regenrohr
DF	Dehnfuge	RWA	Rauch- und Wärmeabzugsanlage
E	Elektro	S	Sanitär
EFH	Erdgeschossfußbodenhöhe	ST	Sturz ab UK Decke
AFL	Feuerlöscher	SW	Schmutzwasser
FBK	Fussbodenkanal	TRH	Treppenhaus
FBS	Fussbodenschlitz	UK	Unterkante
FT	Fertigteil	UZ b/h	Unterzug Breite/Höhe
AH	Heizung	ÜZ b/h	Überzug Breite/Höhe
HK	Heizkörper	VK	Vorderkante
IK	Innenkante	VM	Vormauerung
KS	Kanalsohle		
L	Lüftung		

RAUMSTEMPEL

000	Raumnummer
Raumbezeichnung	
Fläche m²	
RFB	Rohfußboden
FFB	Fertigfußboden
UK RD	Unterkante Rohdecke
UK FD	Unterkante Fertigdecke
FB	Fußbodentyp
BODEN	Bodenbelag
D	Deckenbelag

WANDOBERFLÄCHE

SB "X"	Sichtbeton + Sichtbetonklasse		
A QX	Anstrich + Qualität	STV	Stahlverbund
P	Putz	BW	Beschichtete Wand
H	Holz	F	Fliesen
HPW	Holzprallwand	GW	Glastrennwand
SM	Sichtmauerwerk	HWP	Holzwollplatte

BRANDSCHUTZ

- feuerbeständige Brandwand, EI 90-M (BW F90-A+[M])
- feuerbeständige Wand, Bauart einer Brandwand, EI 90-M (BBW F90-A+[M])
- feuerbeständige Wand, EI 90 (F90-A)
- Oberfläche, Bekleidung und Dämmung aus nb Baustoffen (Baustoffklasse A)
- Wand aus nichtbrennbaren Stoffen (Baustoffklasse A)
- hochfeuerhemmende Wände mit mech. Beanspruchung EI 60-M (F60+[M])
- hochfeuerhemmende Wände, EI 60 (F60)
- feuerhemmende Wände, EI 30 (F30)

TÜREN

T90-RS	Feuerbeständige, rauchdichte und selbstschließende Tür, EI90-S200C5	M	Schiebetür Manuell
T90-D	Feuerbeständige, dicht- und selbstschließende Tür, EI90-SaC5	K	Schiebetür mit Kontakt
T60-RS	Hochfeuerhemmende, rauchdichte und selbstschließende Tür, EI60-S200C5	A	Automatiktür
T60-D	Hochfeuerhemmende, dicht- und selbstschließende Tür, EI60-SaC5	OTS	Obertürschließer
T30-RS	Feuerhemmende, rauchdichte und selbstschließende Tür, EI30-S200C5	ZK	Zutrittskontrolle / Kartenleser
T30-D	Feuerhemmende, dicht- und selbstschließende Tür, EI30-SaC5	DTA	Drehtürantrieb
RS	Rauchdichte und selbstschließende Tür, S200C5	MF	Mechanische Feststellanlage
dTs	Dicht- und selbstschließende Tür, SaC5	EMF	Elektromechanische Feststellanlage
dT	Dichtschließende Tür, [D]	EMAF	Elektromagnetische Feststellanlage
		FTT	Fluchttürterminal

TORE, KLAPPEN

T60-D klappe	Hochfeuerhemmende, dicht- und selbstschließende Klappe /Tor, mit 4-seitig umlaufender Dichtung und Bodenschwelle, EI60-SaC2
T60-RS klappe	Hochfeuerhemmende, rauchdichte und selbstschließende Klappe /Tor, mit 4-seitig umlaufender Dichtung und Bodenschwelle, EI60-S200C2
T90-D klappe	Feuerbeständige, dicht- und selbstschließende Klappe/Tor mit 4-seitig umlaufender Dichtung und Bodenschwelle, EI90-SaC2
T90-RS klappe	Feuerbeständige, rauchdichte und selbstschließende Klappe /Tor, mit 4-seitig umlaufender Dichtung und Bodenschwelle, EI90-S200C2

HINWEIS

Tür- und Brüstungshöhen sind bezogen auf OK FFB!
Alle Ausführungspläne haben nur Gültigkeit in Verbindung mit den Unterlagen des Statikers und aller Fachplaner. Sämtliche Maße sind vom Unternehmer verantwortlich am Bau zu prüfen.
Etwaige Maßdifferenzen sind sofort der zuständigen Bauleitung zu melden!

Index	Änderungsbeschreibung	Datum	Gez.	Gepr.
L	Änderung Wandstärke Schachtwand FWT 3.OG TRH 2, Umplanung Trockenbau Wasserspender Foyer Achse 3 / C-D, Trockenbauplanung FWT 3.OG fortgeschrieben, Durchbrüch ILtS OG1 ergänzt, Durchbruch ILtS OG3 angepasst, Achse 18 / G-H Stahltreppe und Gitterrostpodest ergänzt, Raumstempel LS.03.019 ergänzt,	08.09.2026	wa	

ÜBERSICHTSPLAN

±0.00 = 145.70 m ü.NN

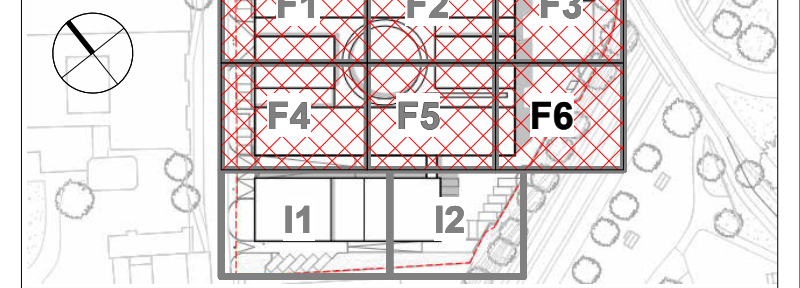

Objekt

Hauptfeuerwache mit Rettungswache
An den Kaiserthermen 1, 54290 Trier

und Integrierte Leitstelle
An den Kaiserthermen 3, 54290 Trier

Massstab: 1 : 50
Datum: 13.05.2026
Gezeichnet: DD
Plannummer - wa: 107
Geprüft: DD
Planname: HFW_F_5_GPOBJ_00_GR_10_F-L

Planinhalt

Hauptfeuerwache mit Rettungswache

Grundriss EG

Projektstatus: Ausführungsplanung
Format: 2378 x 1682 mm

Entwurfsverfasser

wulf architekten gmbh
Breitscheidstraße 8
70174 Stuttgart

t +49 711 248 917-0

Datum, Unterschrift Entwurfsverfasser

Generalplaner / Architekt

wulf architekten gmbh
Breitscheidstraße 8
70174 Stuttgart

t +49 711 248 917-0

Datum, Unterschrift Generalplaner:in / Architekt:in

Bauherr

Stadtverwaltung Trier - Amt für Brand-, Zivilschutz und Rettungsdienst
St. - Barbara - Ufer 40
54290 Trier

t 0651 9488 - 0
f 0651 9488 - 1901

Datum, Unterschrift Projektmanagement

Datum, Unterschrift Amtsleitung

Datum, Unterschrift Dezernat