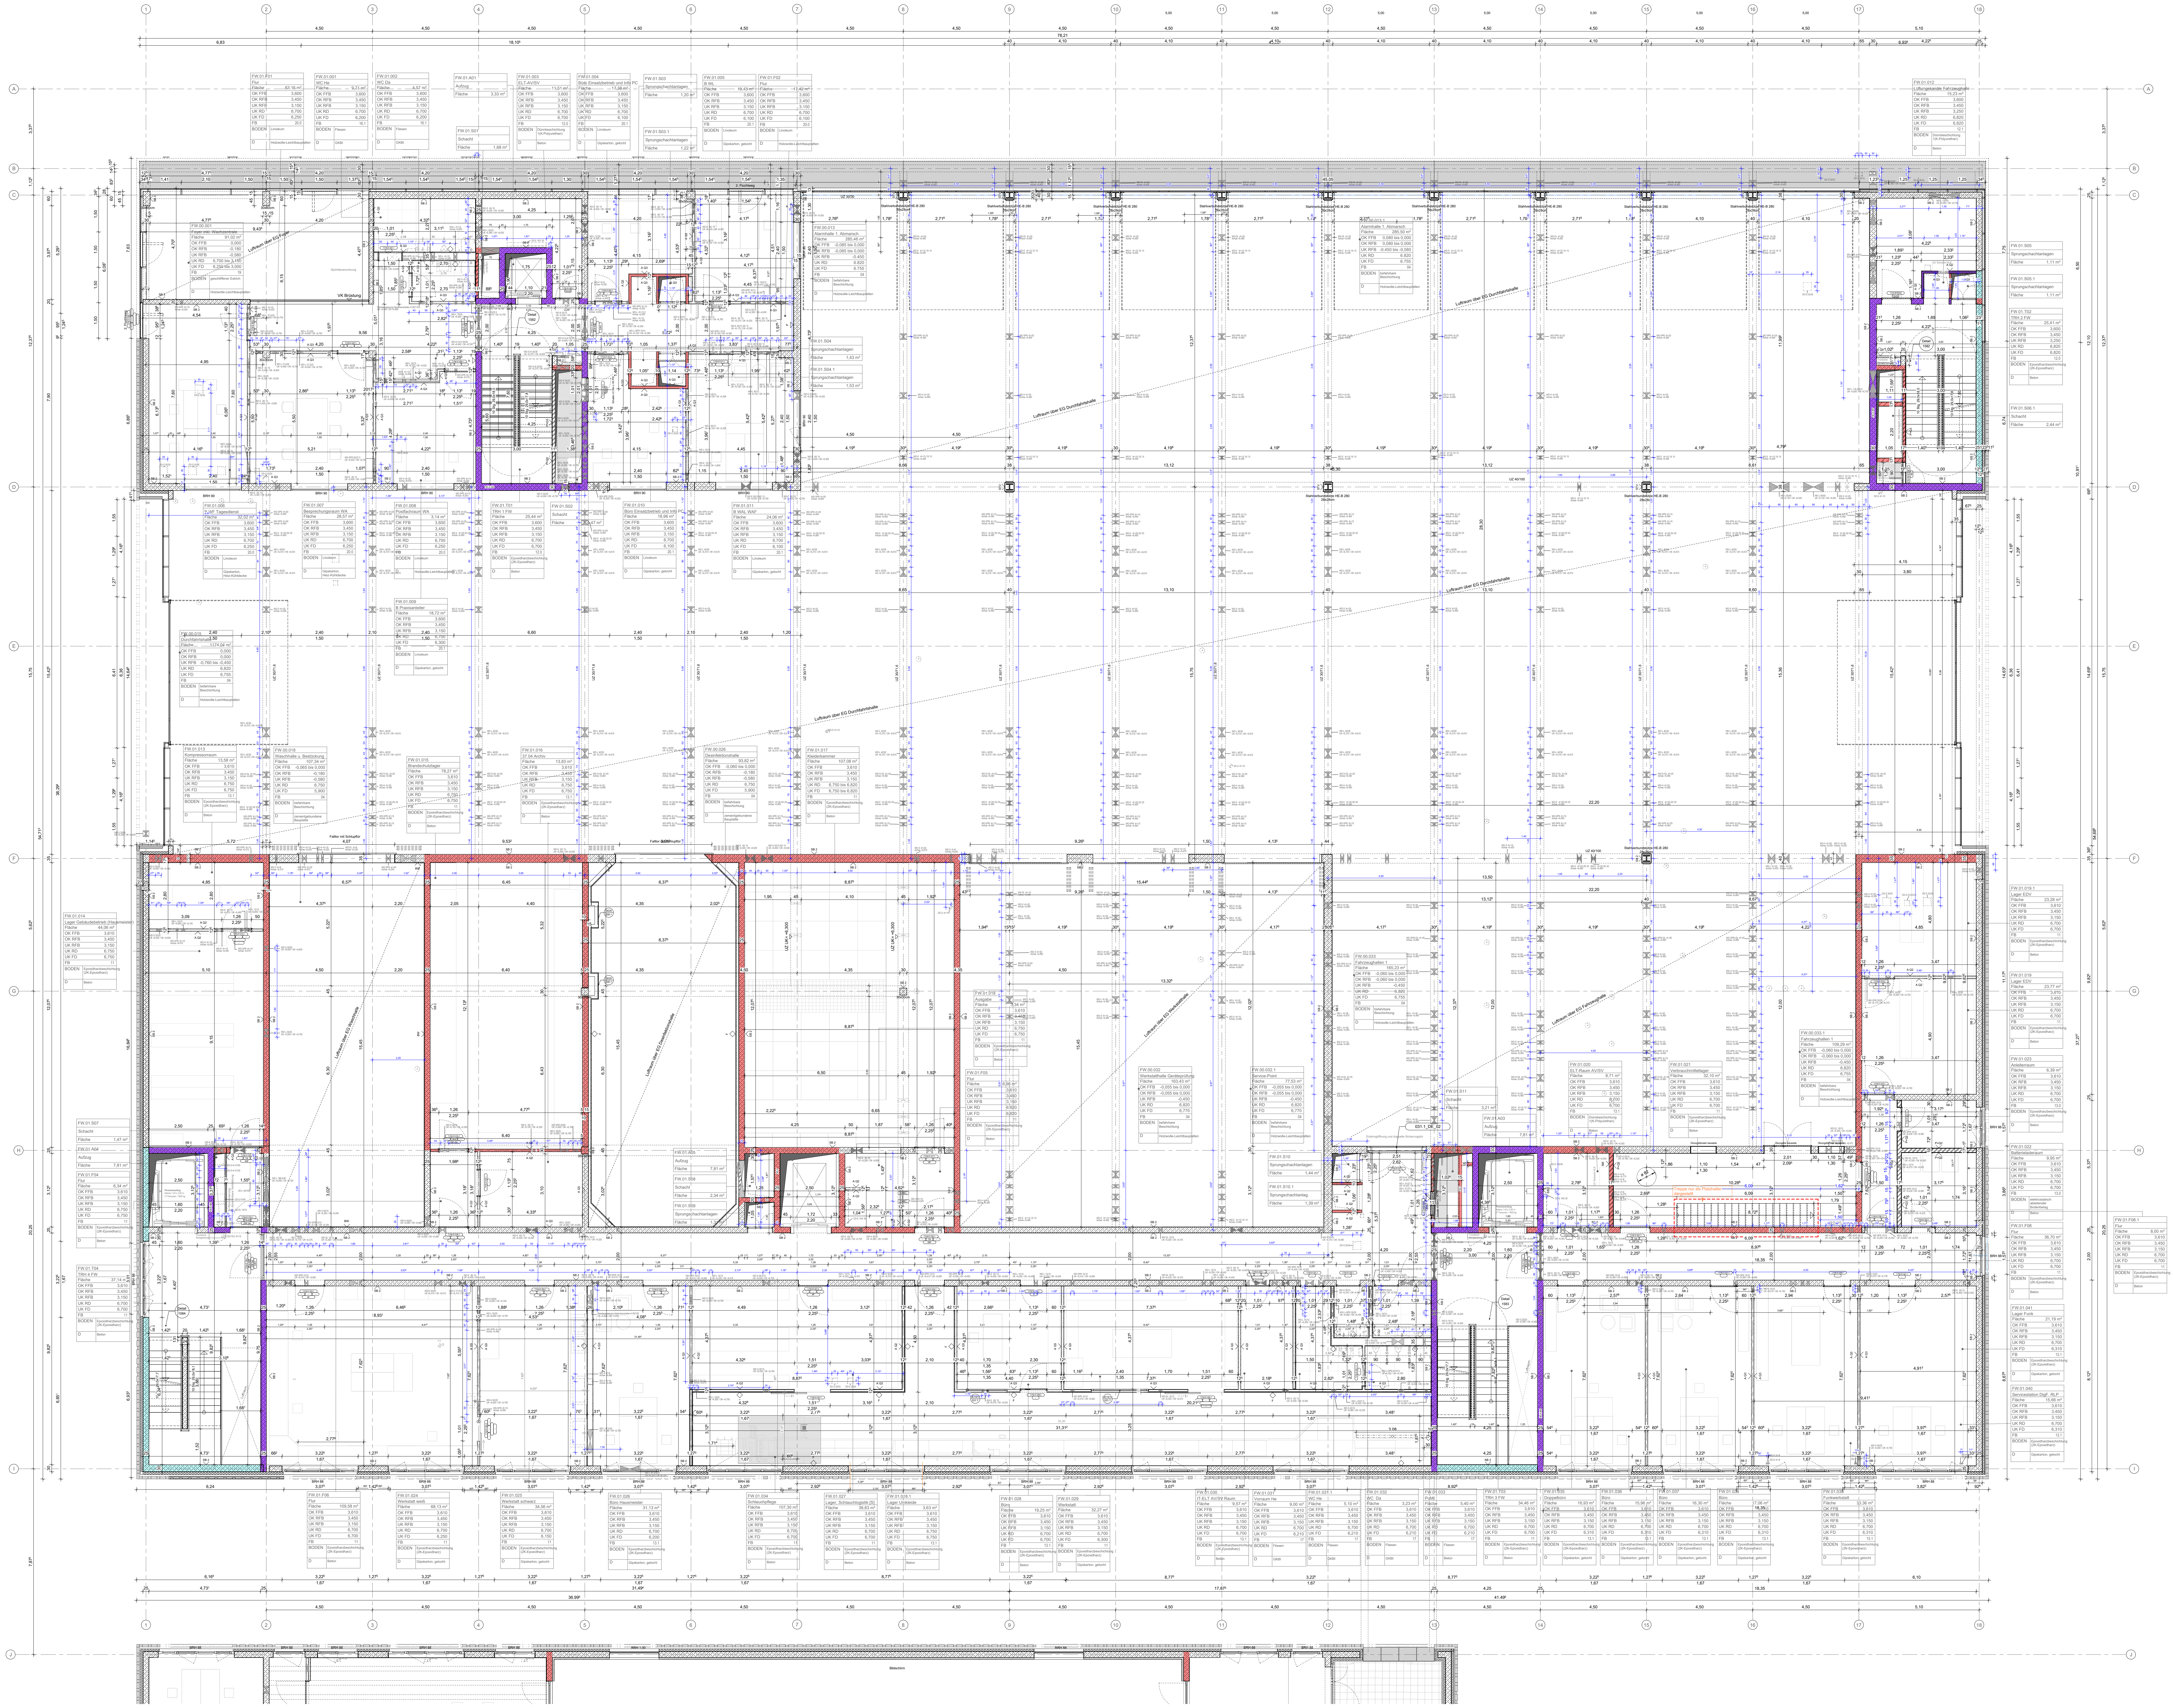

LEGENDE

▨	STB	Stahlbeton	▨	MW Z	Mauerwerk, Ziegel	▨	MW KS	Mauerwerk, Kalksandstein
▨	STB WU	Stahlbeton WU	🟧	GK	Montagewand, Gipskarton	🟥		Grundstücksgrenze
▦	BFT	Stahlbeton-Fertigteil	▨	H	Brettschichtholz, Konstruktionsholz	▨		Dämmziegel

AUSSPARUNGEN

DD (L/B)	Deckendurchbruch	
DS (L/B/H)	Deckenschlitz	
DD (L/B)	Wanddurchbruch - Freigegeben	
DD (L/B)	Wanddurchbruch - ohne Freigabe	
SWS/WWS (L/B/H)	Senkrecher/ Waagrechter Wandschlitz	
BD (L/B)	Bodendurchbruch	
BS (L/B)	Bodenschlitz	
KB (⌀)	Kernbohrung Boden	
KB (⌀)	Kernbohrung Decke	

SYMBOLE SCHNITT

RFB	Rohfußboden
FFB	Fertigfußboden
RFB = FFB	Rohfußboden = Fertigfußboden
UK RD	Unterkante Rohdecke
UK FD	Unterkante Fertigdecke
UK RD = UK FD	Unterkante Rohdecke = Unterkante Fertigdecke

SYMBOLE GRUNDRISS

VK RD	Vorderkante Rohdecke
VK FD	Vorderkante Fertigdecke
Höhenkote	FFB RFB
Detailverweis	DET --- Detail Detailnummer

ABKÜRZUNGEN

AK	Aussenkante	LH	Lichte Höhe
B ...	Boden	NRWG	Natürliches Rauch- und Wärmeabzugsgerät
BA	Bodenablauf	OK	Oberkante
BRH	Brüstungshöhe ab FFB	RA	Öffnung zur Rauchableitung
D ...	Decke	RH	Rohhöhe
DE	Dacheinlauf	RR	Regenrohr
DF	Dehnfuge	RWA	Rauch- und Wärmeabzugsanlage
E	Elektro	S	Sanitär
EFH	Erdgeschossfußbodenhöhe	ST	Sturz ab UK Decke
AFL	Feuerlöscher	SW	Schmutzwasser
FBK	Fussbodenkanal	TRH	Treppenhaus
FBS	Fussbodenschlitz	UK	Unterkante
FT	Fertigteil	UZ b/h	Unterzug Breite/Höhe
AH	Heizung	ÜZ b/h	Überzug Breite/Höhe
HK	Heizkörper	VK	Vorderkante
IK	Innenkante	VM	Vormauerung
KS	Kanalsohle		
L	Lüftung		

RAUMSTEMPEL

000	Raumnummer
Raumbezeichnung	
Fläche m²	
RFB	Rohfußboden
FFB	Fertigfußboden
UK RD	Unterkante Rohdecke
UK FD	Unterkante Fertigdecke
FB	Fußbodentyp
BODEN	Bodenbelag
D	Deckenbelag

WANDOBERFLÄCHE

SB "X"	Sichtbeton + Sichtbetonklasse		
A QX	Anstrich + Qualität	STV	Stahlverbund
P	Putz	BW	Beschichtete Wand
H	Holz	F	Fliesen
HPW	Holzprallwand	GW	Glastrennwand
SM	Sichtmauerwerk	HWP	Holzwollplatte

BRANDSCHUTZ

▭	feuerbeständige Brandwand, EI 90-M (BW F90-A+[M])
🟪	feuerbeständige Wand, Bauart einer Brandwand, EI 90-M (BBW F90-A+[M])
🟥	feuerbeständige Wand, EI 90 (F90-A)
🟦	Oberfläche, Bekleidung und Dämmung aus nb Baustoffen (Baustoffklasse A)
🟦	Wand aus nichtbrennbaren Stoffen (Baustoffklasse A)
🟧	hochfeuerhemmende Wände mit mech. Beanspruchung EI 60-M (F60+[M])
🟧	hochfeuerhemmende Wände, EI 60 (F60)
🟨	feuerhemmende Wände, EI 30 (F30)

TÜREN

T90-RS	Feuerbeständige, rauchdichte und selbstschließende Tür, EI2 90-S200C5	M	Schiebetür Manuell
T90-D	Feuerbeständige, dicht- und selbstschließende Tür, EI2 90-SaC5	K	Schiebetür mit Kontakt
T60-RS	Hochfeuerhemmende, rauchdichte und selbstschließende Tür, EI2 60-S200C5	A	Automatiktür
T60-D	Hochfeuerhemmende, dicht- und selbstschließende Tür, EI2 60-SaC5	OTS	Obertürschließer
T30-RS	Feuerhemmende, rauchdichte und selbstschließende Tür, EI2 30-S200C5	ZK	Zutrittskontrolle / Kartenleser
T30-D	Feuerhemmende, dicht- und selbstschließende Tür, EI2 30-SaC5	DTA	Drehtürantrieb
RS	Rauchdichte und selbstschließende Tür, S200C5	MF	Mechanische Feststellanlage
dTs	Dicht- und selbstschließende Tür, SaC5	EMF	Elektromechanische Feststellanlage
dT	Dichtschließende Tür, [D]	EMAF	Elektromagnetische Feststellanlage
		FTT	Fluchttürterminal

TORE, KLAPPEN

T60-D klappe	Hochfeuerhemmende, dicht- und selbstschließende Klappe /Tor, mit 4-seitig umlaufender Dichtung und Bodenschwelle, EI2 60-SaC2
T60-RS klappe	Hochfeuerhemmende, rauchdichte und selbstschließende Klappe /Tor, mit 4-seitig umlaufender Dichtung und Bodenschwelle, EI2 60-S200C2
T90-D klappe	Feuerbeständige, dicht- und selbstschließende Klappe/Tor mit 4-seitig umlaufender Dichtung und Bodenschwelle, EI2 90-SaC2
T90-RS klappe	Feuerbeständige, rauchdichte und selbstschließende Klappe /Tor, mit 4-seitig umlaufender Dichtung und Bodenschwelle, EI2 90-S200C2

HINWEIS

Tür- und Brüstungshöhen sind bezogen auf OK FFB!
Alle Ausführungspläne haben nur Gültigkeit in Verbindung mit den Unterlagen des Statikers und aller Fachplaner. Sämtliche Maße sind vom Unternehmer verantwortlich am Bau zu prüfen.
Etwaige Maßdifferenzen sind sofort der zuständigen Bauleitung zu melden!

Index	Änderungsbeschreibung	Datum	Gez.	Gepr.
H	Überarbeitung Raumstempel, Trockenbauplanung fortgeschrieben	06.08.2026	wa	

ÜBERSICHTSPLAN

±0.00 = 145.70 m ü.NN

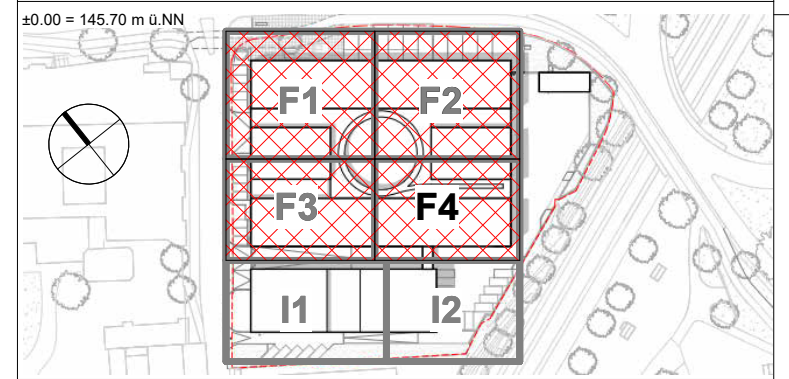

Objekt **Hauptfeuerwache mit Rettungswache** An den Kaiserthermen 1, 54290 Trier **und Integrierte Leitstelle** An den Kaiserthermen 3, 54290 Trier	Massstab 1 : 50 Datum 03.06.2026 Gezeichnet DD Plannummer - wa 115 Geprüft DD Planname HFW_F_5_GPOBJ_01_GR_10_F-H
Planinhalt **Hauptfeuerwache mit Rettungswache** **Grundriss OG1**	Projektstatus Ausführungsplanung Format 2378 x 1682 mm
Entwurfsverfasser **wulf architekten gmbh** Breitscheidstraße 8 70174 Stuttgart t +49 711 248 917-0	Datum, Unterschrift Entwurfsverfasser
Generalplaner / Architekt **wulf architekten gmbh** Breitscheidstraße 8 70174 Stuttgart t +49 711 248 917-0	Datum, Unterschrift Generalplaner:in / Architekt:in
Bauherr **Stadtverwaltung Trier - Amt für Brand-, Zivilschutz und Rettungsdienst** St. - Barbara - Ufer 40 54290 Trier t 0651 9488 - 0 f 0651 9488 - 1901	Datum, Unterschrift Projektmanagement Datum, Unterschrift Amtsleitung Datum, Unterschrift Dezernat